



DETALLES DE INSTALACION APARATOS

ESCALA N/A


SANITARIO

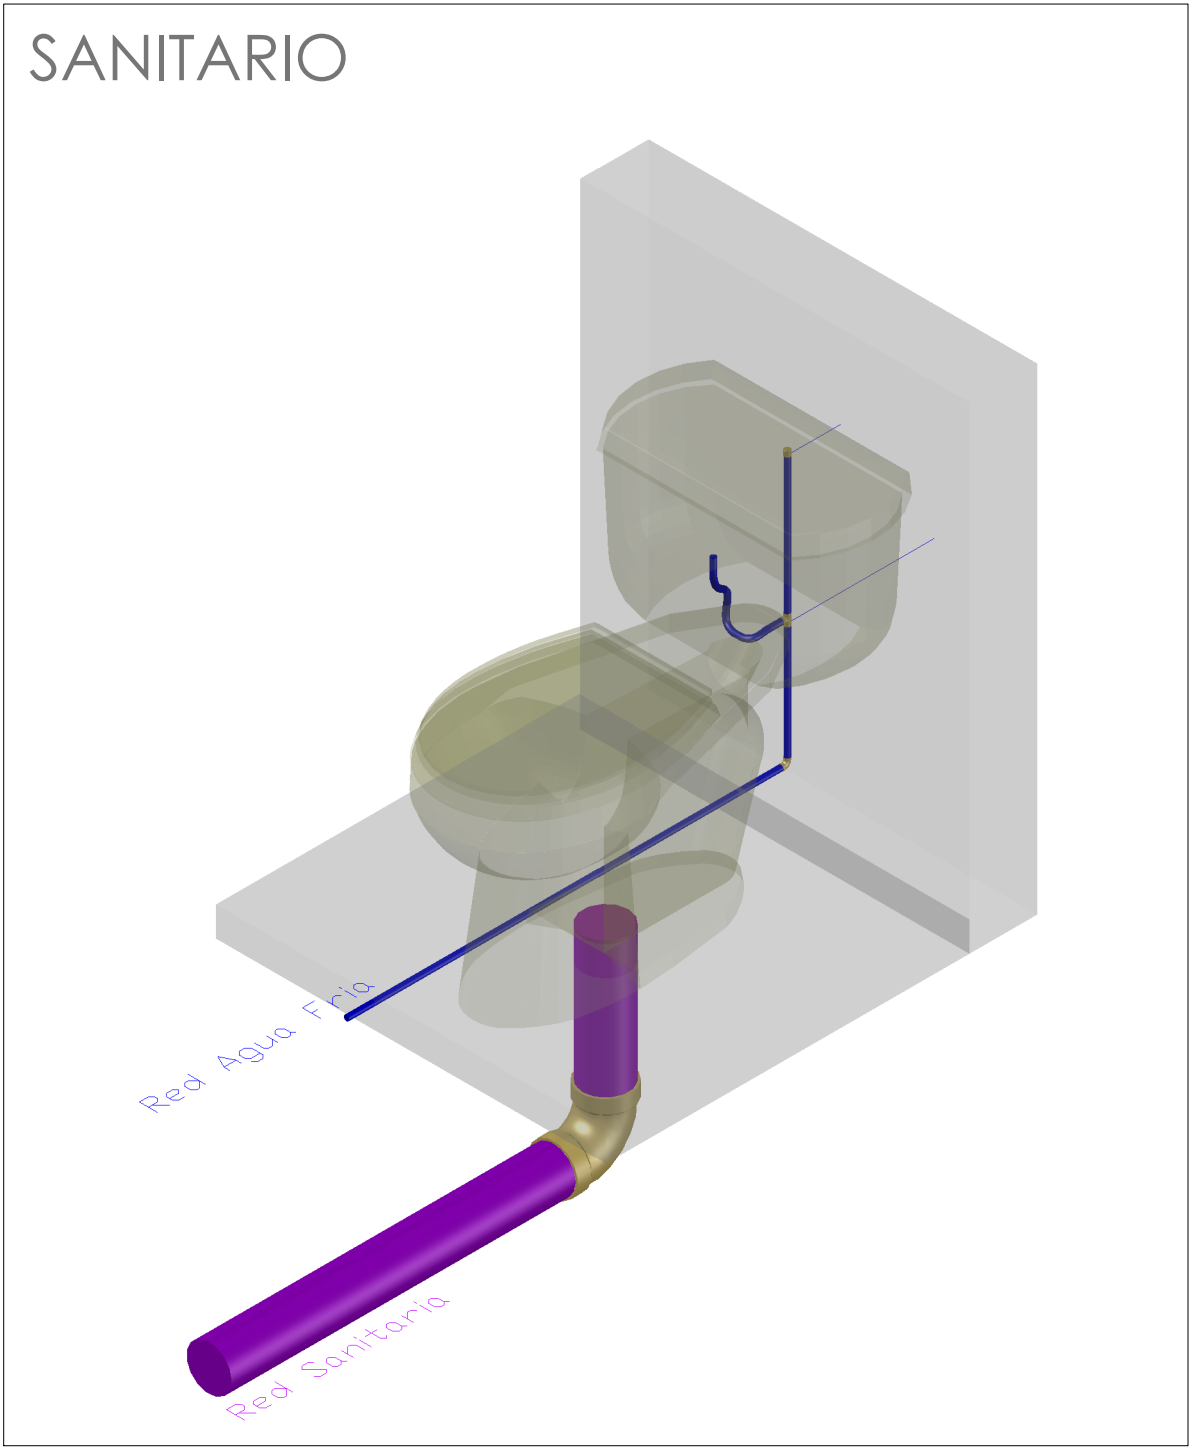


LAVAMANOS

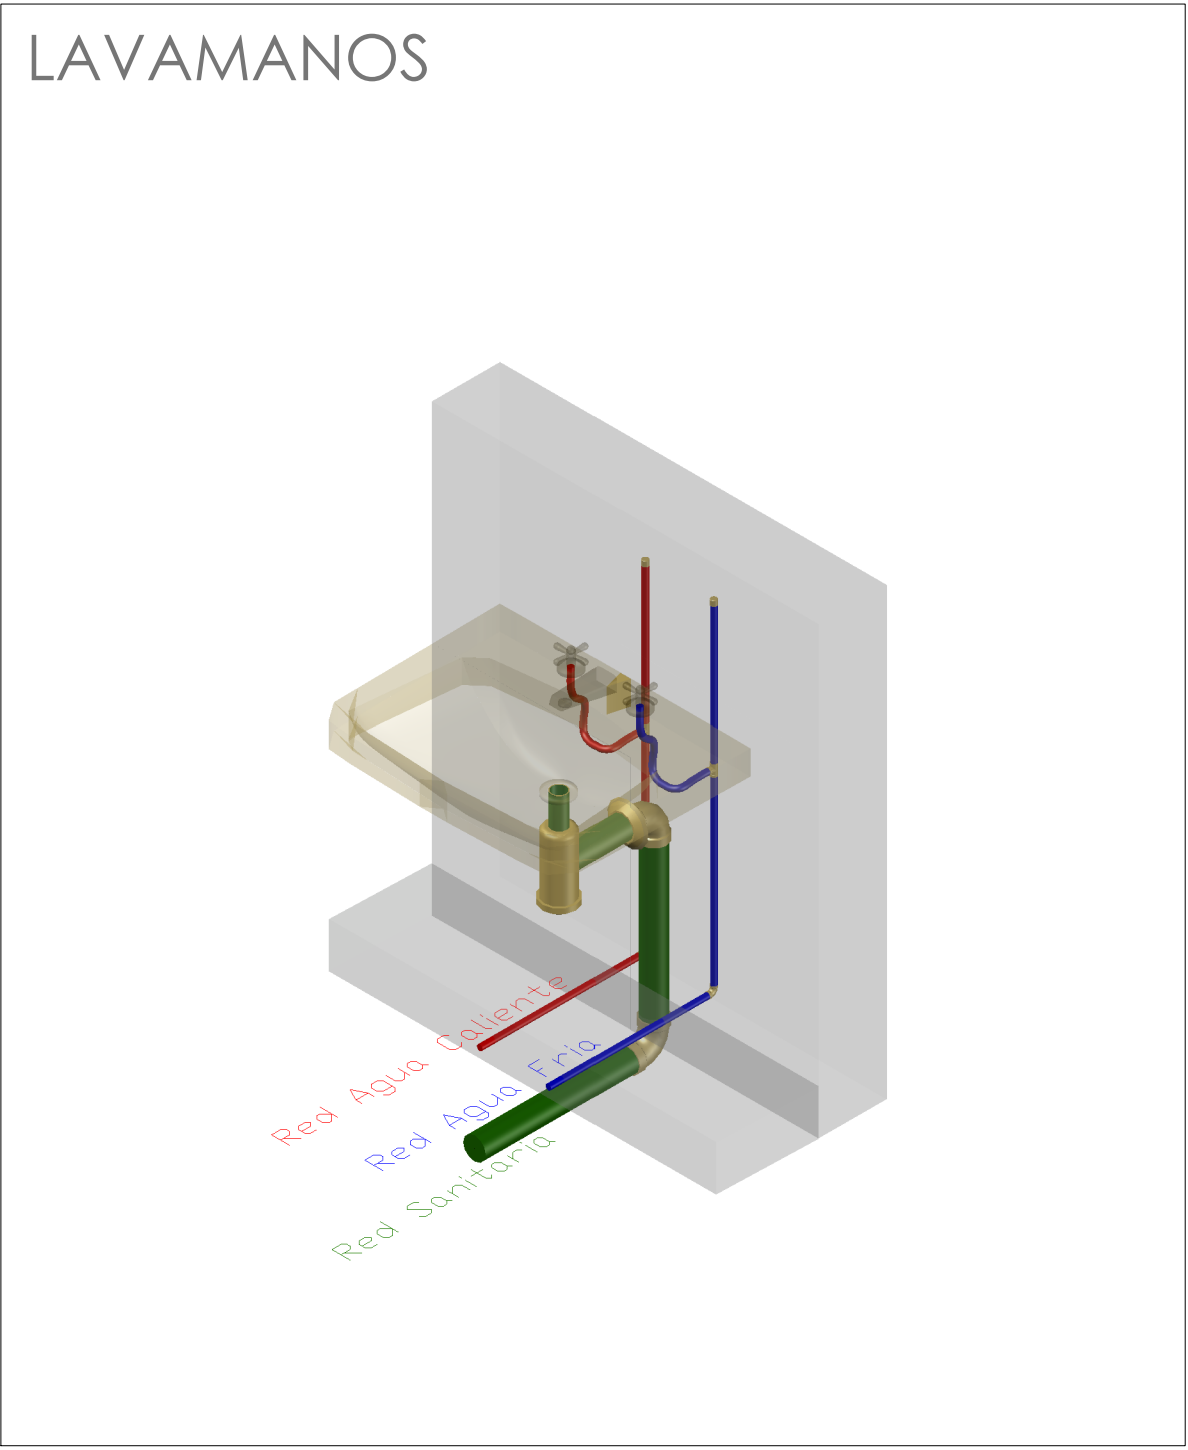


LAVAPLATOS

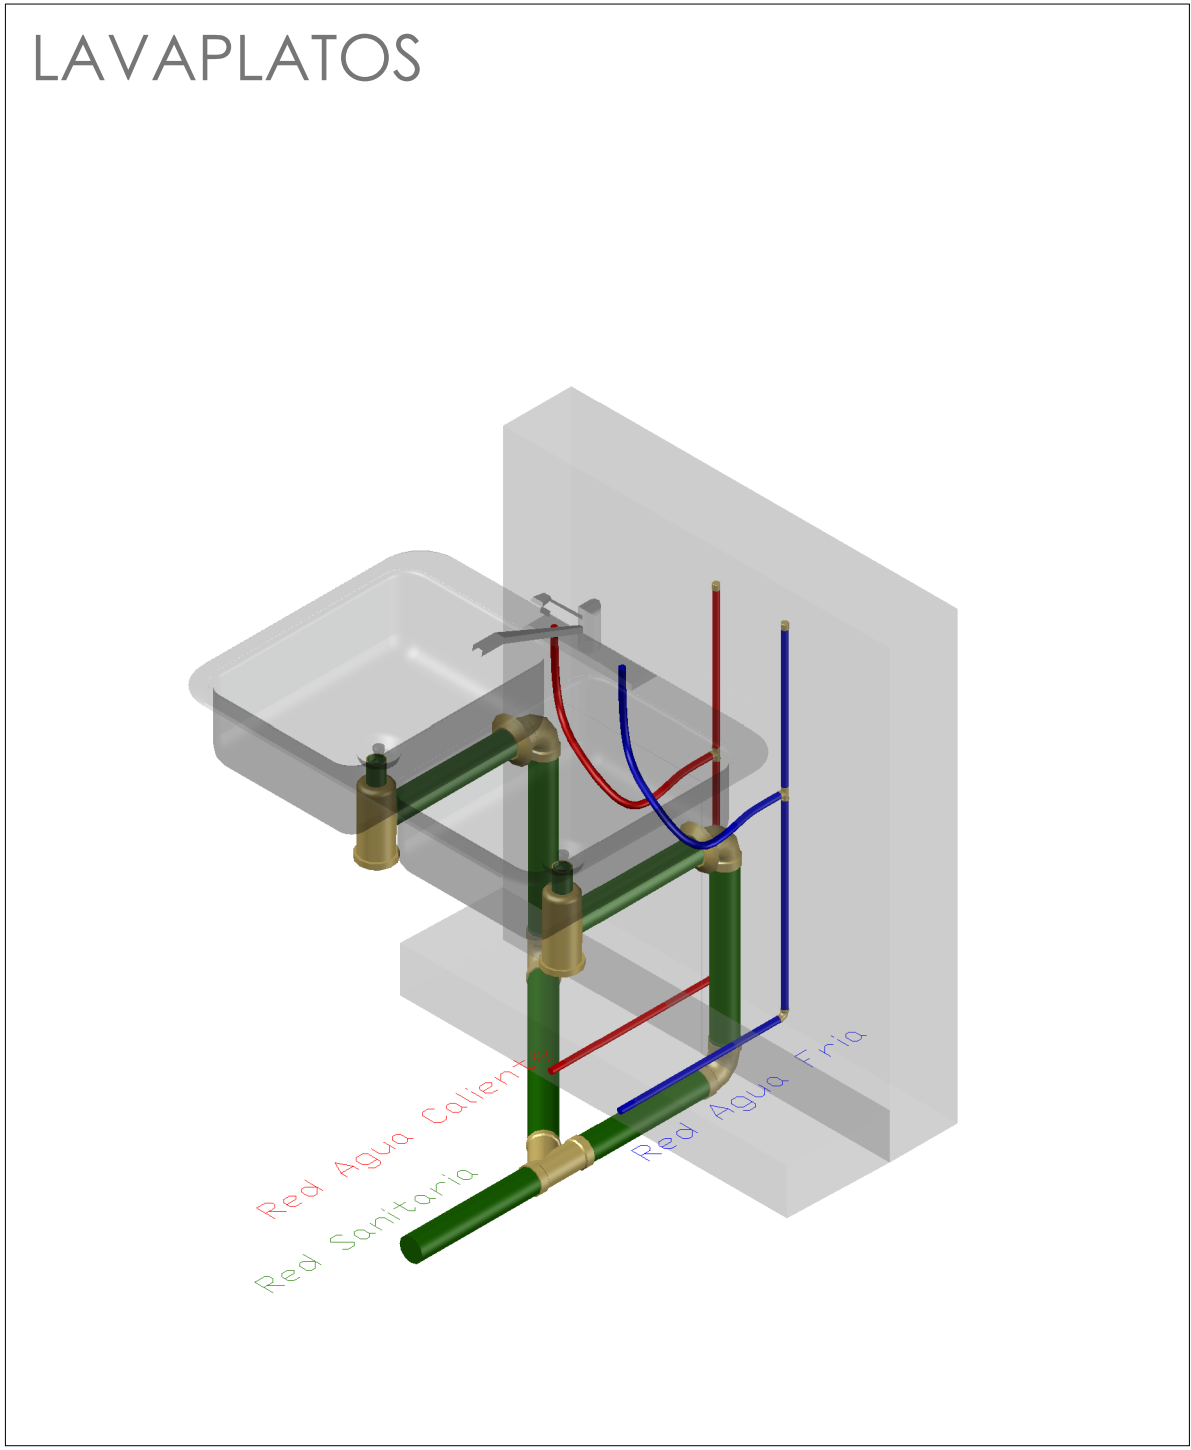


DUCHA

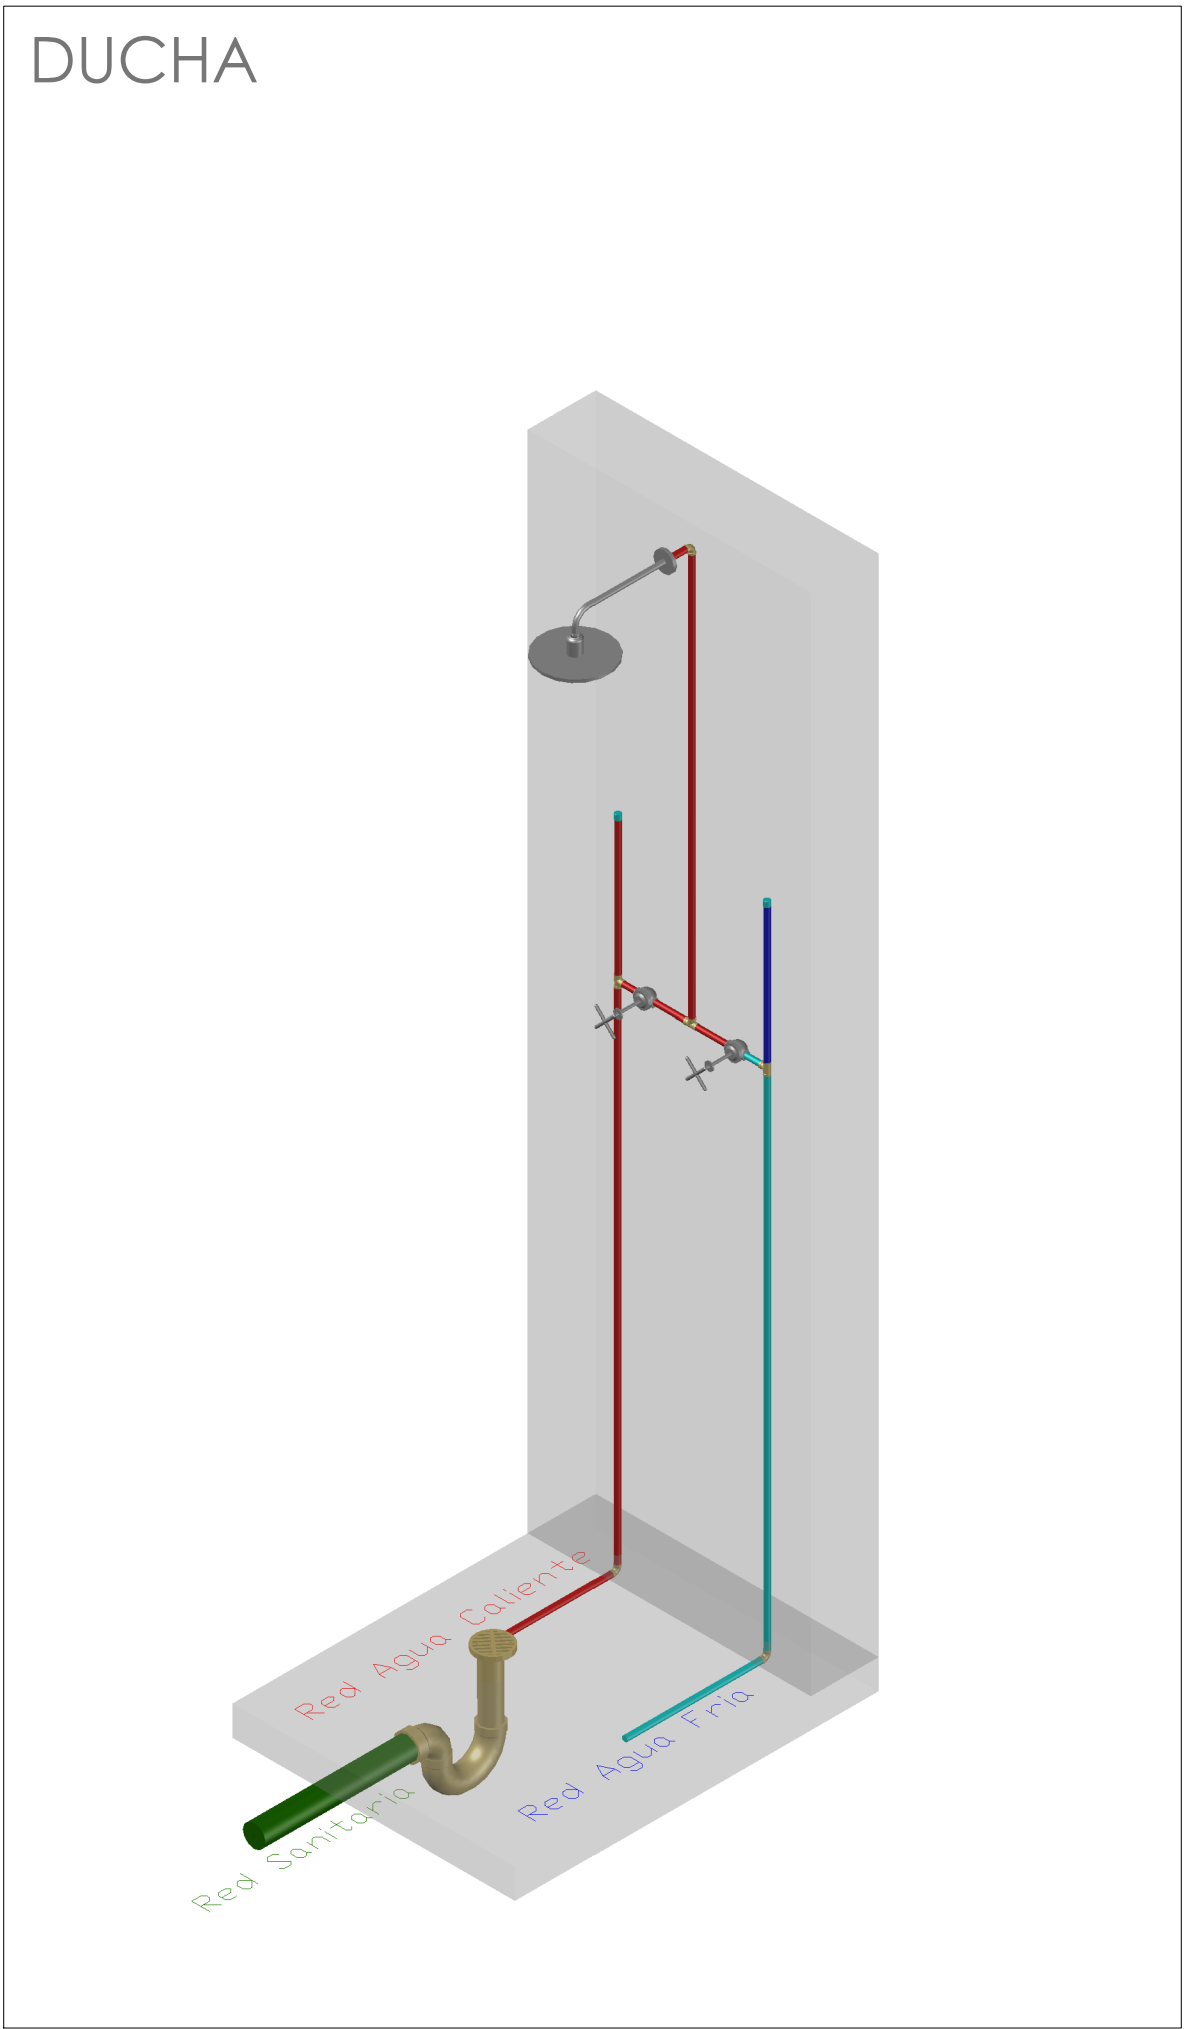


LAVADERO

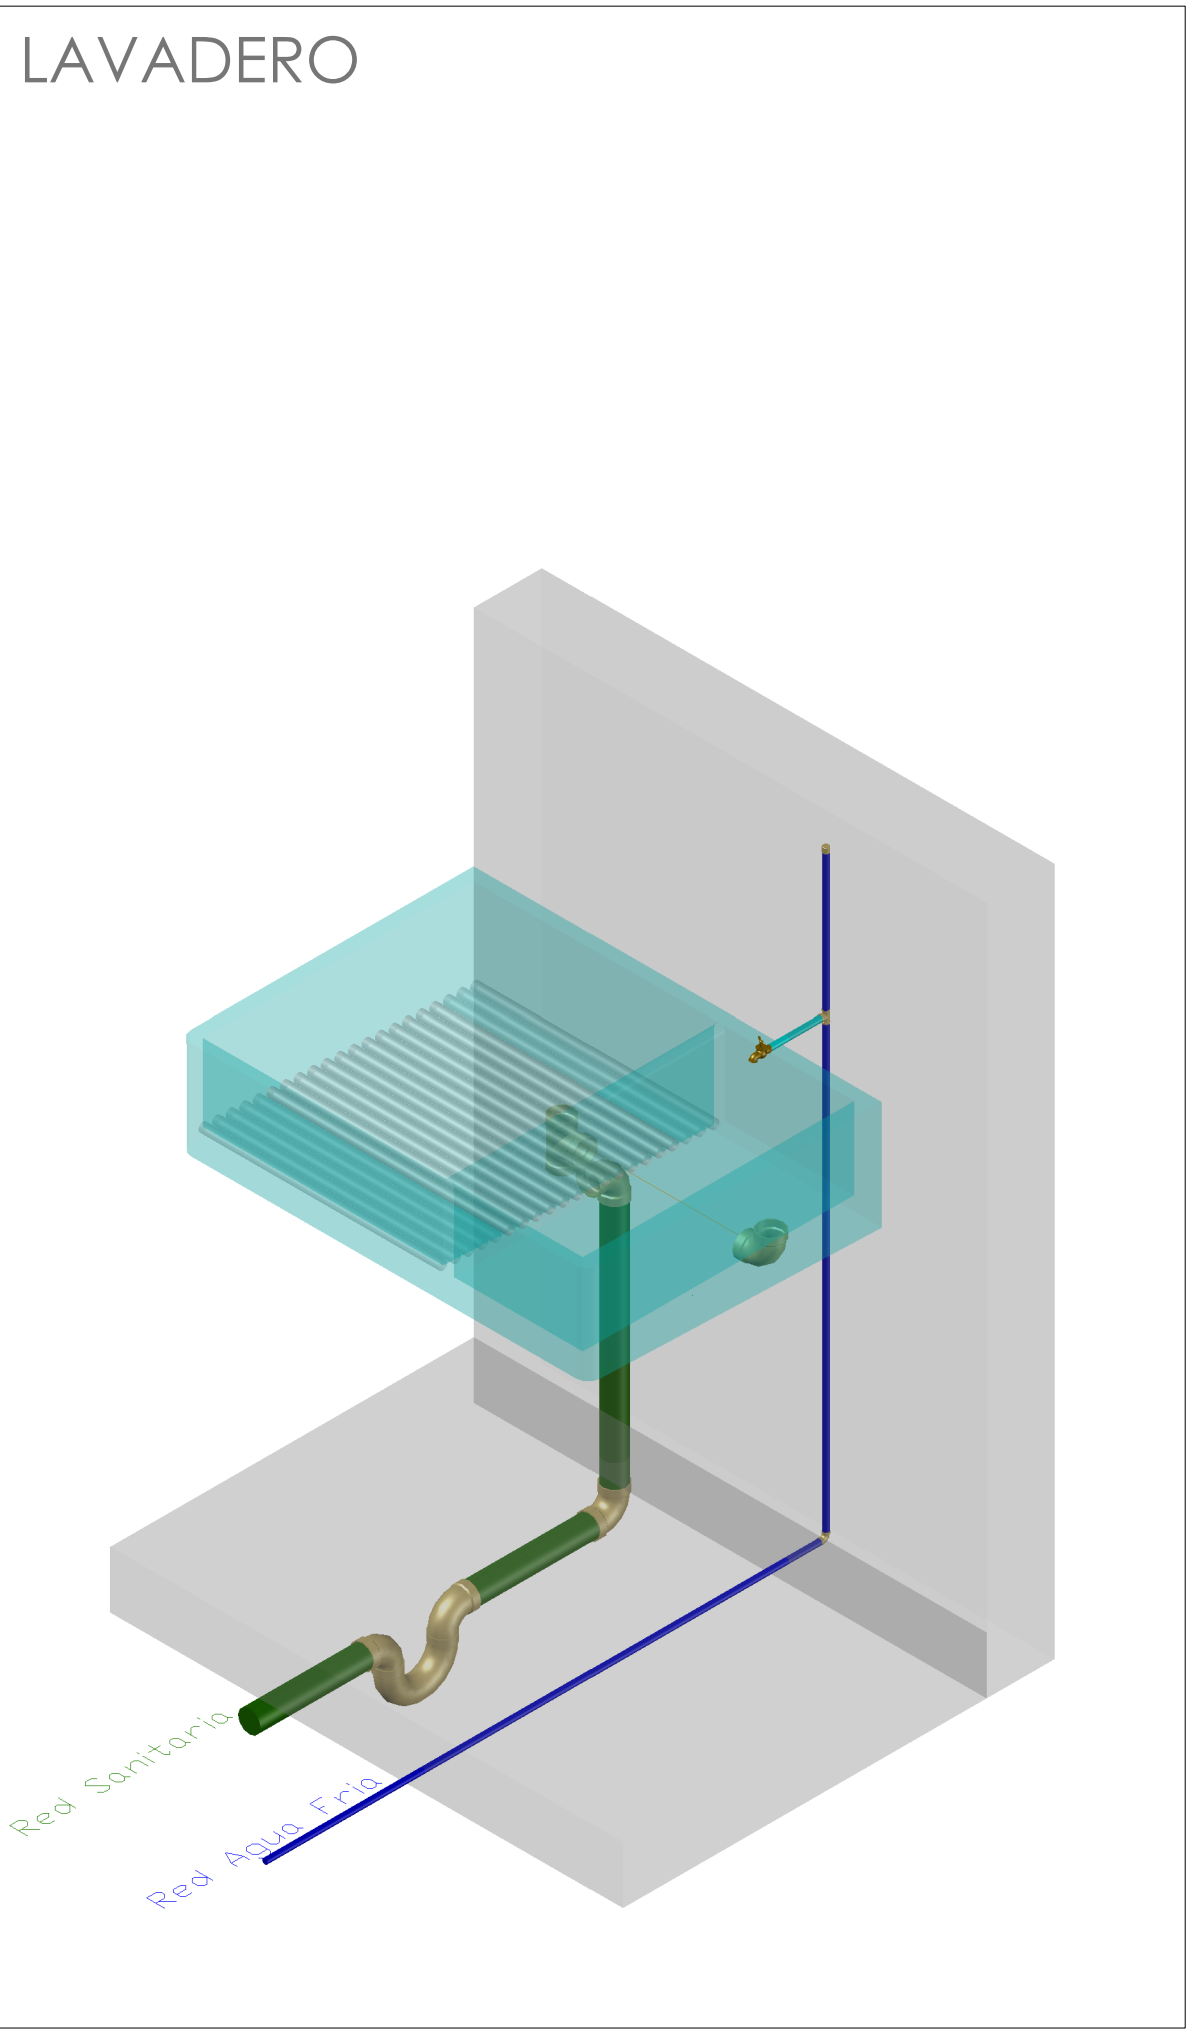


CALENTADOR

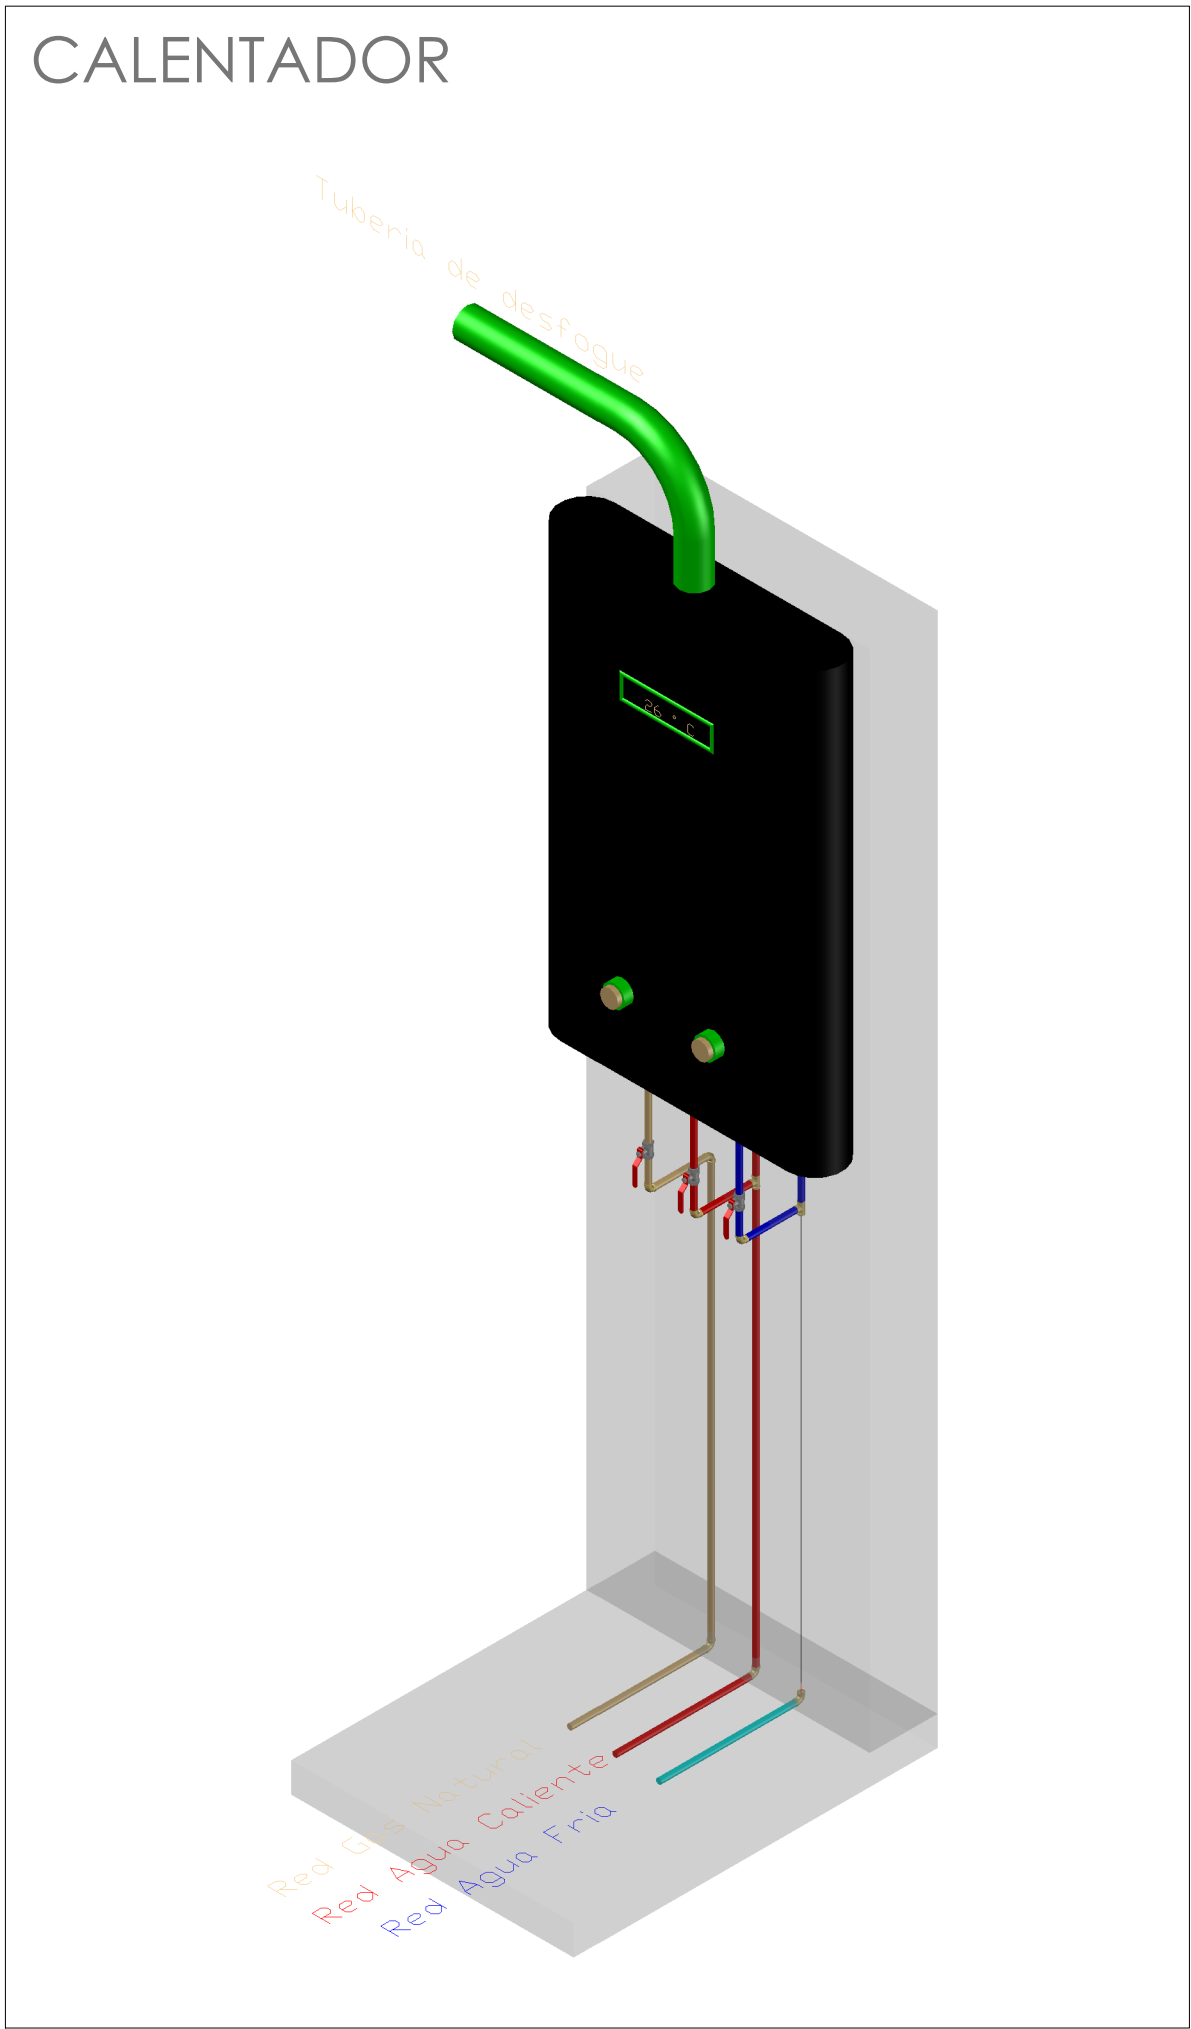

LAVADORA

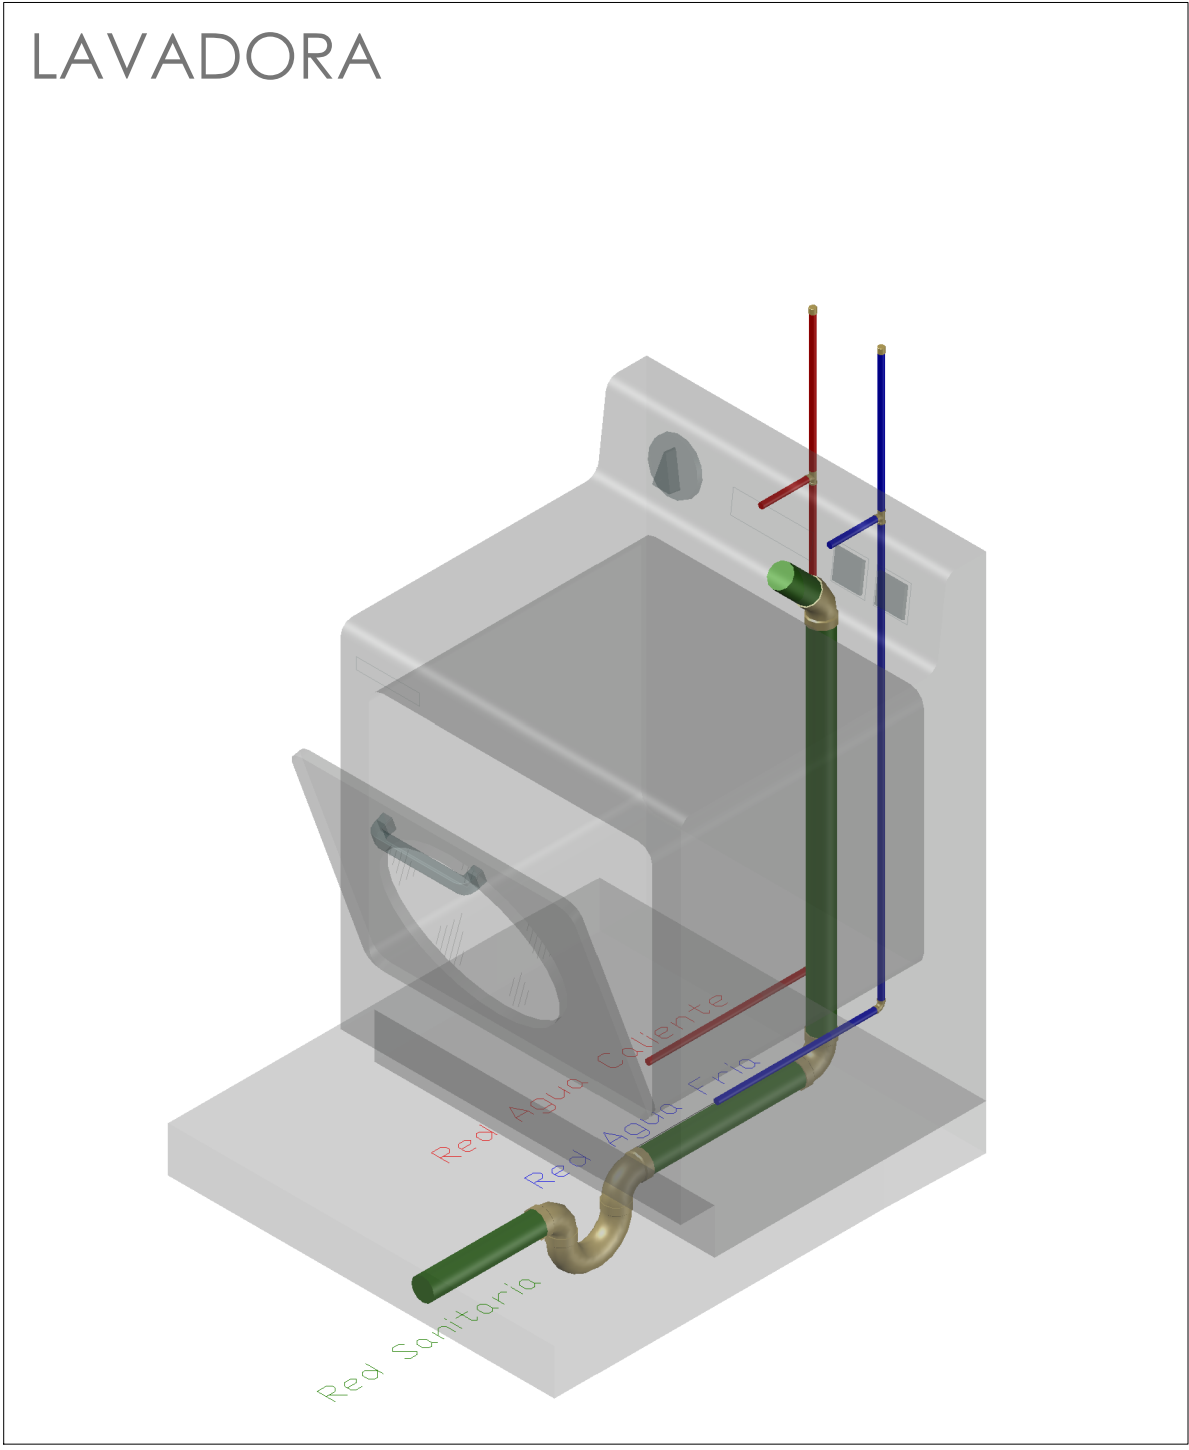

REVENTILACION

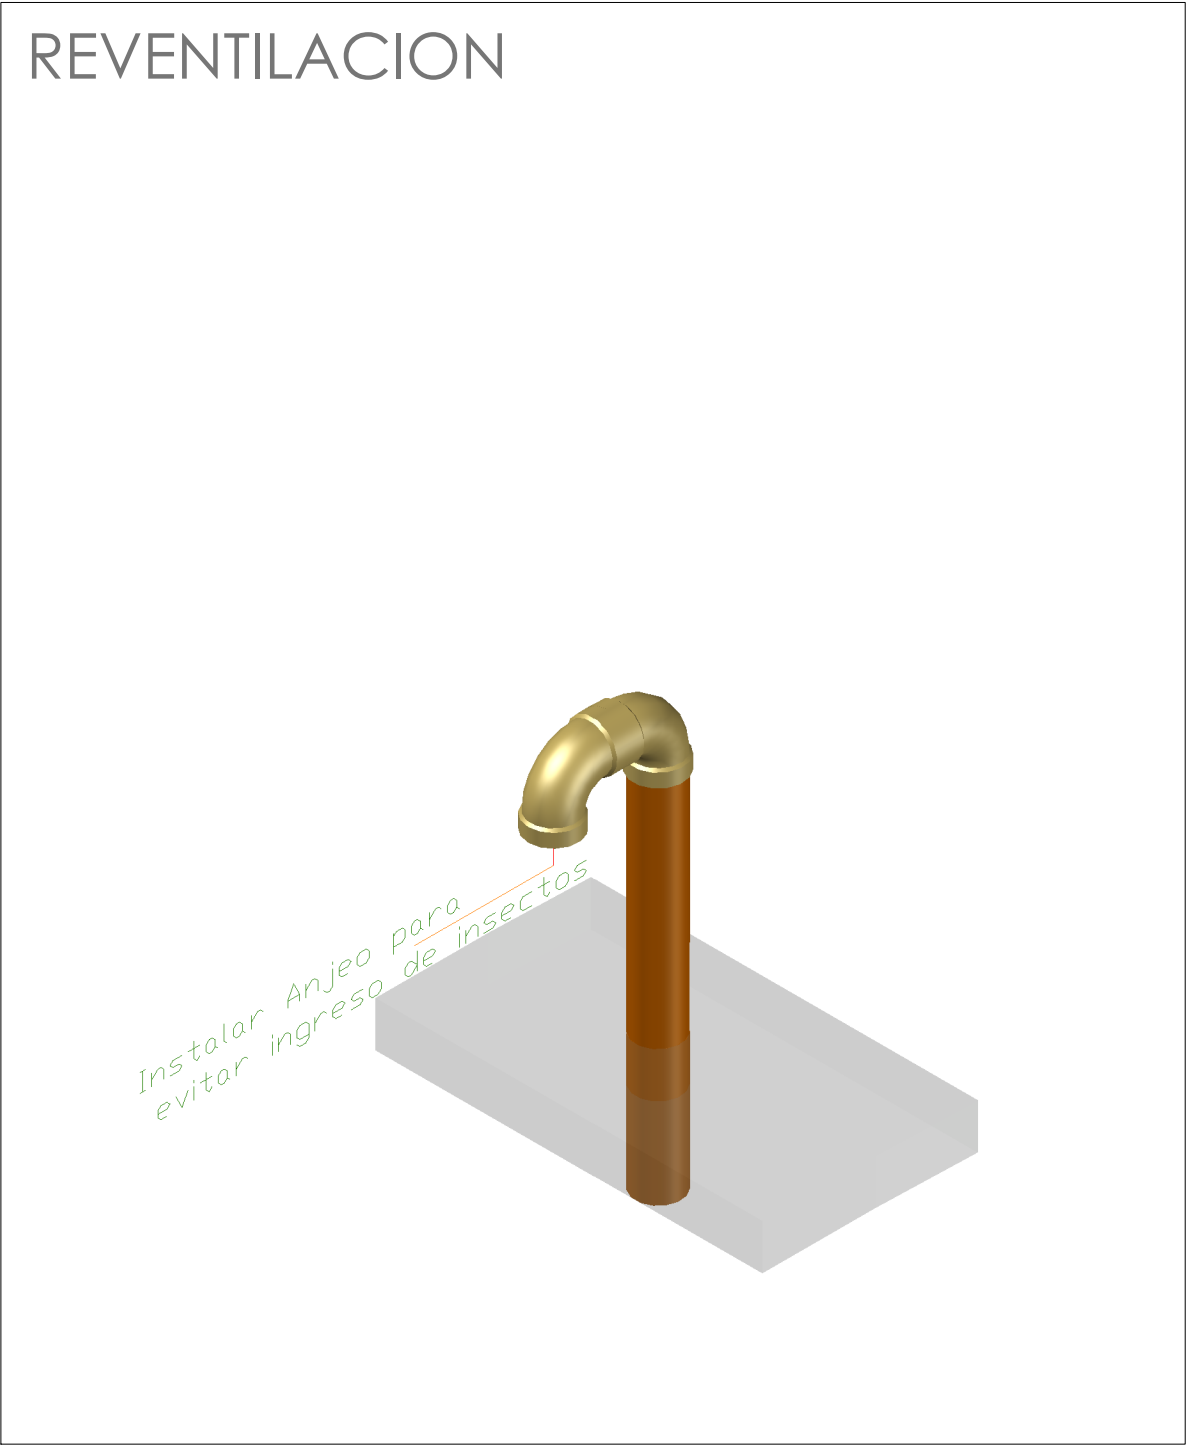

SIFON / CAMPANA

